

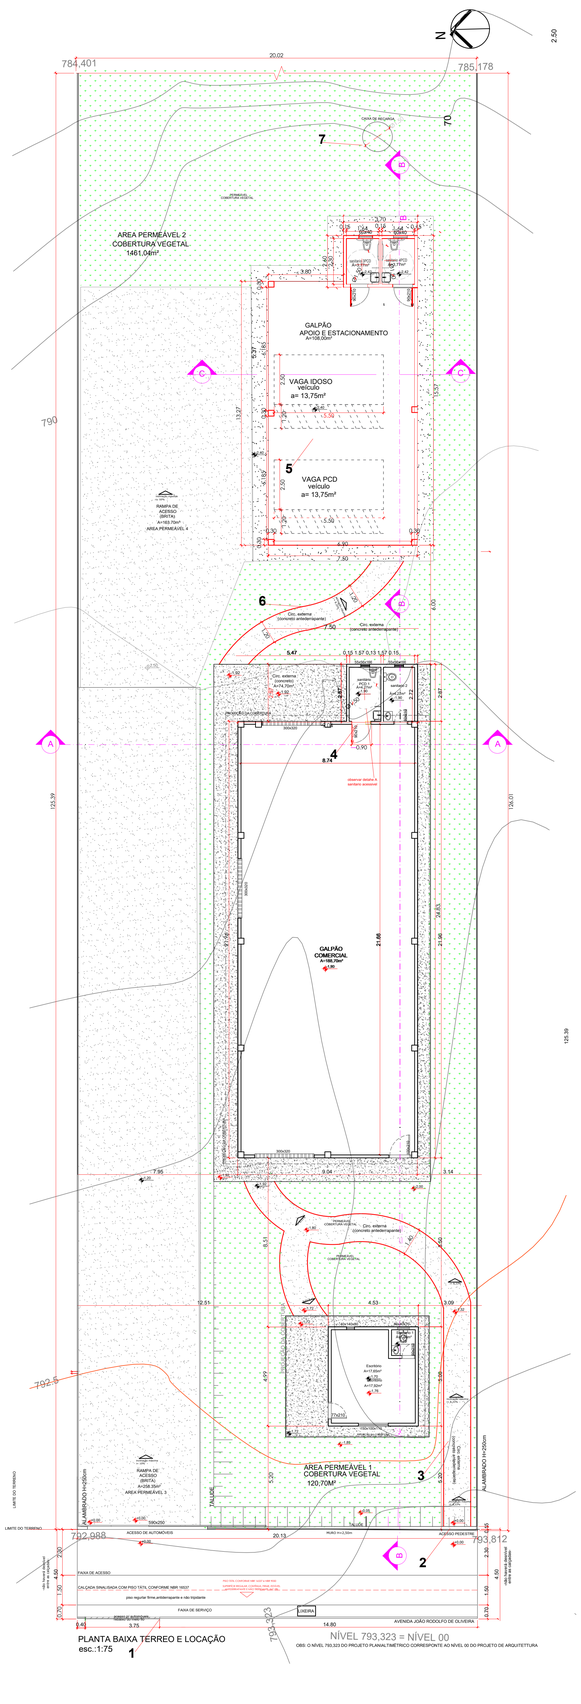


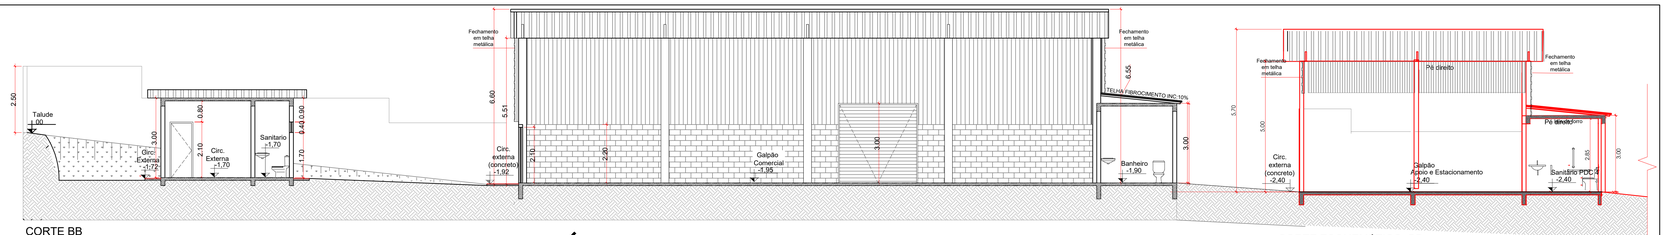


CORTE BB
esc.:1:75


CORTE ESQUEMÁTICO BB

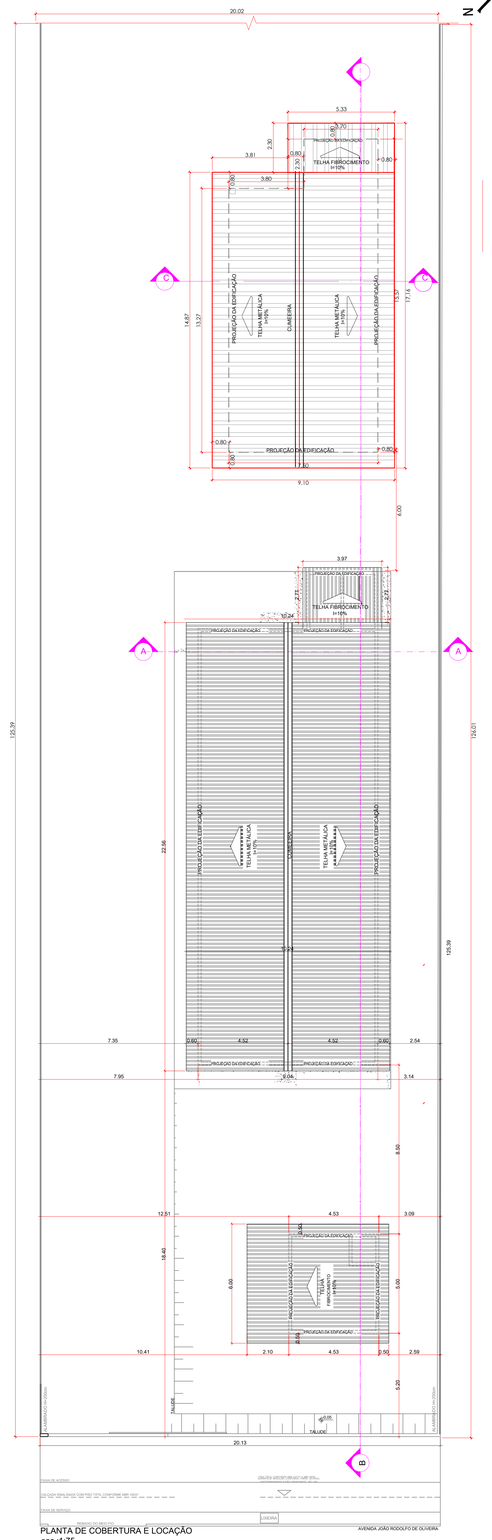

PLANTA DE COBERTURA E LOCAÇÃO
esc.:1:75

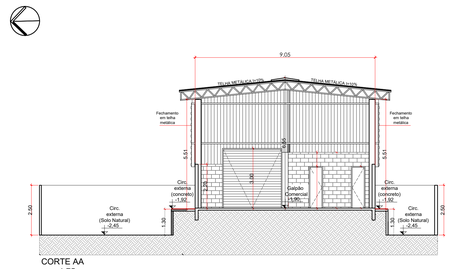

CORTE AA
esc.:1:75

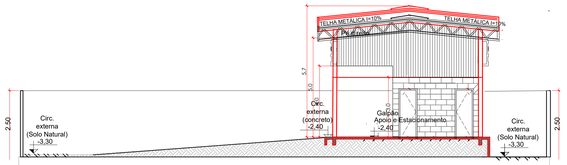

CORTE ESQUEMATICO CC
esc.:1:75

MODIFICAÇÕES:
1- REBAIXO DO MEIO FIO PARA ACESSO DE CARROS - DIMINUIR PARA 3,75m
2- PORTÃO DE ACESSO DE PEDESTRE
3- RAMPA DE ACESSO DE PEDESTRE
4- ADAPTAR SANITARIO DO GALPÃO EXISTENTE (PDC)
5- GALPÃO DE ESTACIONAMENTO COM 2 VAGAS ACESSÍVEIS E 2 SANITÁRIOS ACESSÍVEIS (PDC)
6- CRIAR RAMPA DE ACESSO DO GALPÃO EXISTENTE AO GALPÃO DE ESTACIONAMENTO
7- EXECUTAR CAIXA DE INFILTRAÇÃO

DETALHE A SANITÁRIO PDC

No projeto de arquitetura a ser aprovado deverá constar o cálculo e o detalhe do poço de infiltração, bem como SEU ESQUEMA DE COLETA DAS AGUAS PLUVIAIS E O DIRECIONAMENTO DO FLUXO AO POÇO DE INFILTRAÇÃO.
É NECESSÁRIO 1m³ DE CAIXA DE RECARGA PARA CADA 200,00m² DE TERRENO IMPERMEABILIZADO SUPERFÍCIE MÍNIMA 1,00m² PROFUNDIDADE MÁXIMA 2,60m

VOLUME NECESSÁRIO = 510,81m² /200m² = 200,00m² CORRESPONDE A 1,00m³
510,81m² CORRESPONDE A 2,55m³


VOLUME TOTAL = Pi x R² x H
Pi= 3,14
R = raio= 0,80m
H= altura= 2,36m

VOLUME TOTAL = 3,14x0,64x2,36
VOLUME TOTAL = 4,74m³

VOLUME TOTAL DE 1 CAIXA=4,74m³
ÁREA DE INFILTRAÇÃO
Fundo do caixa x quantidade = 2,09x1 = 2,09m²



NOTA: A CAIXA DE RECARGA TERÁ TAMANHO MINIMO DE 4,70m³

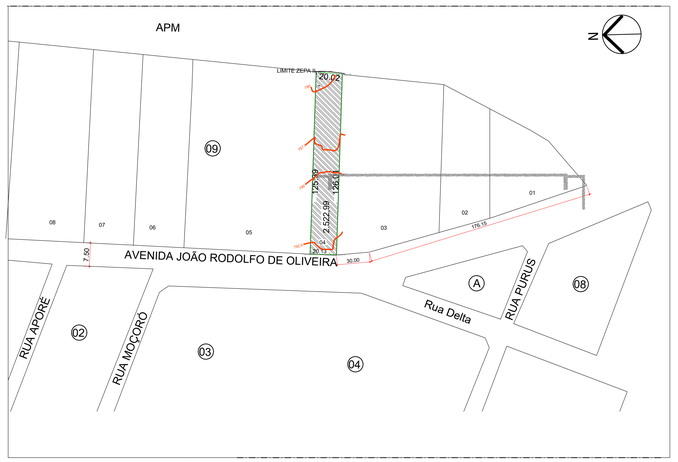

PLANTA DE SITUAÇÃO
esc.:1:1000

* OBSERVAÇÃO:

NOTA: A CAIXA DE INFILTRAÇÃO (RECARGA) SERÁ EXECUTADA
DE ACORDO COM A LEI COMPLEMENTAR Nº 246, DE 29 DE ABRIL DE 2013
SOB A RESPONSABILIDADE DO PROFISSIONAL RESPONSÁVEL PELA EXECUÇÃO DA OBRA

MEMORIAL DE CÁCLULO PARA CAIXA DE INFILTRAÇÃO	
AREA PERMEÁVEL =	1.581,74m²
AREA IMPERMEÁVEL =	941,25 m²
SE PARA CADA 200M² É NECESSARIO 1M³ DE CAIXA DE INFILTRAÇÃO PARA 941,25 m² MINIMO=	4,70m³

LEGGENDA	
	CONSTRUIR
	DEMOLIR
	PERMANECER

QUADRO DE ÁREAS

(m²)	Área	Taxa de ocupação e/índice (%)
Área const. térreo	108,00 m²	
Área á const. térreo	242,96 m²	
Área Total construída	350,96m²	13,91%
Área permeável	1.581,74m²	62,69%
Área impermeável	941,25 m²	
Quantidade de poço de infiltração	2,60 m³	
Área da diretriz viária		
Área do terreno	2.522,99 m²	100%

NOTA: OS SANITÁRIOS PCD ATENDEN A NBR 9050 / 20 (RAIO MÁXIMO DE 50M)

NOTA: PROJETO ATENDERÁ NA ÍNTEGRA TODAS AS NORMAS DE ACESSIBILIDADE VIGENTES.

LEIS REGULAMENTARES:
Lei Complementar nº 124-2016 - Dispõe sobre o Plano Diretor do Município;
Lei Complementar Municipal 152/2018 - Dispõe sobre Uso e Ocupação do Solo; e alterações posteriores;
Lei Municipal 171/2019 - Código de Obras Edificações;
Art. 9º A aprovação dos projetos, o licenciamento de obras, a sua execução, manutenção e conservação, serão reguladas pelo presente Código, pelas normas regulamentares editadas por Decreto Municipal, obedecidas as normas federais e estaduais relativas à matéria e, as normas da Associação Brasileira de Normas Técnicas - ABNT.
Art. 71º Caberá ao proprietário e ao autor do projeto a garantia respectiva ao conforto, à salubridade das edificações e às normas de acessibilidade, quando exigido para o uso do imóvel.

O proprietário declara estar ciente de que inadequações do projeto ou da execução poderão acarretar na suspensão ou cancelamento da licença de projeto e/ou alvará de construção e também no embargo da obra, e até mesmo eventuais demolições. A aprovação do projeto não implica no reconhecimento do direito de propriedade do terreno por parte da prefeitura.

ALVARÁ SIMPLIFICADO

Rev. 21/04/2022

Nº PROTOCOLO: 2023088189

APROVADO
SECRETARIA MUNICIPAL DE PLANEJAMENTO E REGULAÇÃO URBANA

EM ___/___/___

LICENÇA DE PROJETO Nº

IMPORTANTE
Após a conclusão da obra requerer ao Município a Certidão de Conclusão de Obra. Consiste em documento obrigatório comprobatório da conclusão da obra, em conformidade com a Licença de Projeto.

ARQUITETURA MODIFICAÇÃO COM ACRÉSCIMO

COMERCIAL - TÉRREO

ENDEREÇO: AVENIDA JOAO RODOLFO DE OLIVEIRA E AVENIDA NOBERTO JOSE TEIXEIRA, QUADRA 009, LOTE 0004, PARQUE INDUSTRIAL APARECIDA VICE-PRESIDENTE JOSE DE ALENCAR APARECIDA DE GOIÂNIA - GOIÁS

PROPRIETÁRIO: RODOLUG TRANSPORTES LTDA
CNPJ: 07.329.786/0002-15

AUTOR DO PROJ.: SHEILA GONÇALVES DE CASTRO SELLANI
ARQUITETA E URBANISTA CAU - 00A1475894

R.T.: SHEILA GONÇALVES DE CASTRO SELLANI
ARQUITETA E URBANISTA CAU - 00A1475894

ÁREA TERRENO	ÁREA PERMEÁVEL	POÇO DE INFILTRAÇÃO	ÁREA TOTAL CONSTRUÇÃO	Nº PAVIMENTOS	ESCALA	DATA
2.522,99 m²	1.581,74m²	4,70m³	350,96m²	01	INDICADA	29/09/2023

SHEILA CASTRO SELLANI
ARQUITETA E URBANISTA
Fones: 62 996923671

CONTEÚDO:
PLANTA BAIXA TÉRREA E LOCAÇÃO
PLANTA DE COBERTURA E LOCAÇÃO
CORTE AA
CORTE BB
CORTE CC
PLANTA DE SITUAÇÃO

QUADRO DE ÁREAS:
ÁREA DE ACEITE 242,96m²
ÁREA DO ACRÉSCIMO 108,00m²
ÁREA TOTAL CONSTRUÇÃO 350,96m²

PRANCHA: ÚNICA